



Design Portfolio

By Tanya Dhir



ABOUT ME

I design spaces that are meant to be experienced, not just seen.

I am an architect with over 2 years of experience working across national and international projects in architecture, interior design, and landscape design. My work explores the relationship between space, emotion and perception, focusing on creating environments that feel immersive, intuitive, and meaningful.

I am driven by curiosity to blur boundaries between inside and outside, built form and nature using light, material, and spatial flow to shape how people experience space.

 **tanyadhiro2@gmail.com**

 **+1 647-867-7813**

 **Vancouver, BC**

PROFESSIONAL EXPERIENCE

2025- 2026 : Landscape Designer at Paul Sangha Creative

Worked on ultra-high-end residential and commercial projects across Canada, the United States and the United Arab Emirates. Contributed to the planning, design development, and execution of luxury landscape projects, collaborating with multidisciplinary teams to deliver innovative and client-focused outdoor environments.

2022- 2023 : Architect at Hastaakshar Designs Pvt. Ltd.

Contributed to the successful delivery of end-to-end architecture and interior projects, ensuring seamless translation of design intent into built reality across all project stages.

2022 : Student Intern at Raj Rewal Associates

Built understanding of construction methods and detailing by studying project execution drawings and applying that knowledge in studio work.

2021 : Student Intern at Kritarc Designs Pvt. Ltd.

Assisted in translating rough sketches and discussions into workable drawings, learning to align creative ideas with practical construction requirements.

SOFTWARES

Revit	
AutoCad	
VectorWorks	
SketchUp	
Lumion	
Rhino	
Grasshopper	
VRay	
3Ds Max	
Adobe Photoshop	
Adobe Indesign	
Adobe Illustrator	
Microsoft Office	

SKILLS

Visualization
Analysis
Team Work
AI Proficiency
Graphic Presentation

EDUCATION


Advanced Project Management & Strategic Leadership:
Lambton College, CA

Bachelor's of Architecture :
Jamia Millia Islamia, IN


LANGUAGES

English (Proficient)	Punjabi (Intermediate)
Hindi (Native)	German (Basic)

TABLE OF CONTENT

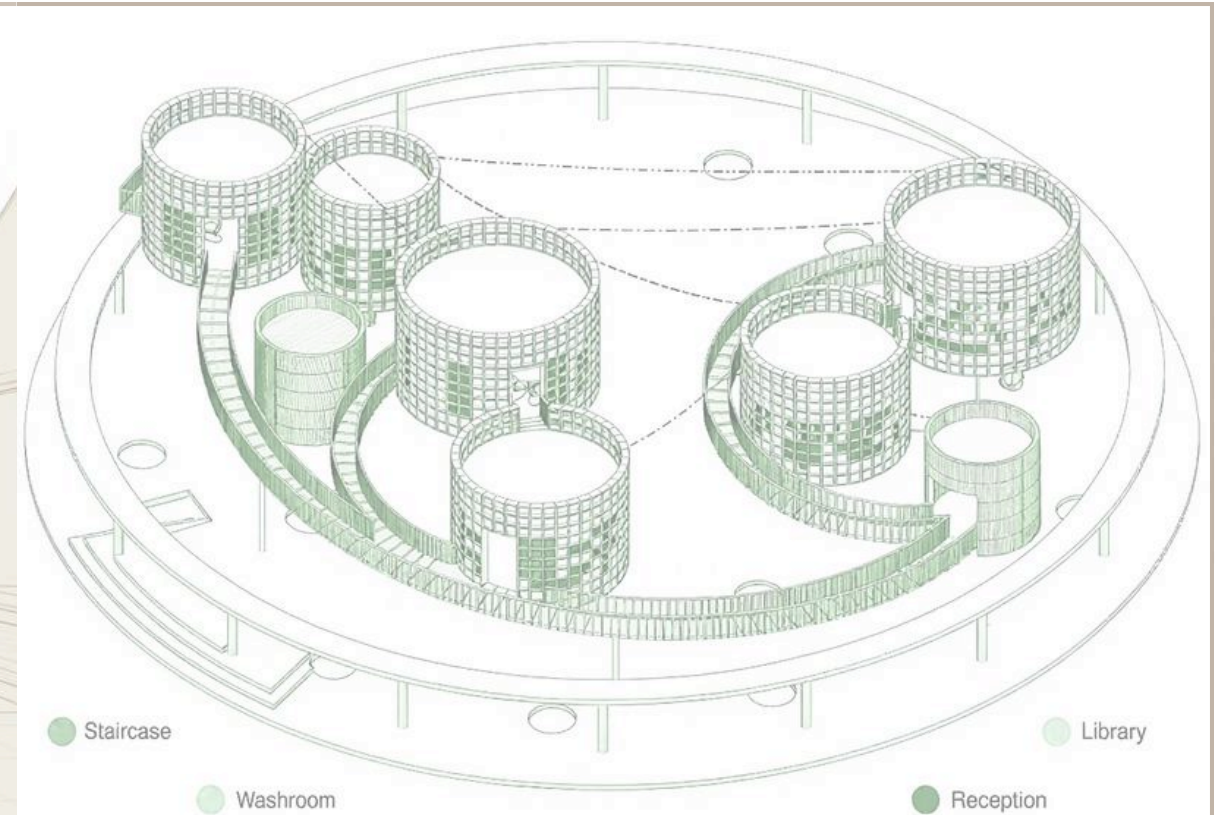

- 01 Selected Professional Experience : Private Residence- Waterfront, Vancouver
- 02 Selected Professional Experience : Private Residence- Delta, BC
- 03 Selected Professional Experience : Private Residence- Vancouver, BC
- 04 Internship Work
- 05 Competition Entry Sheet
- 06 Freelance Design Project

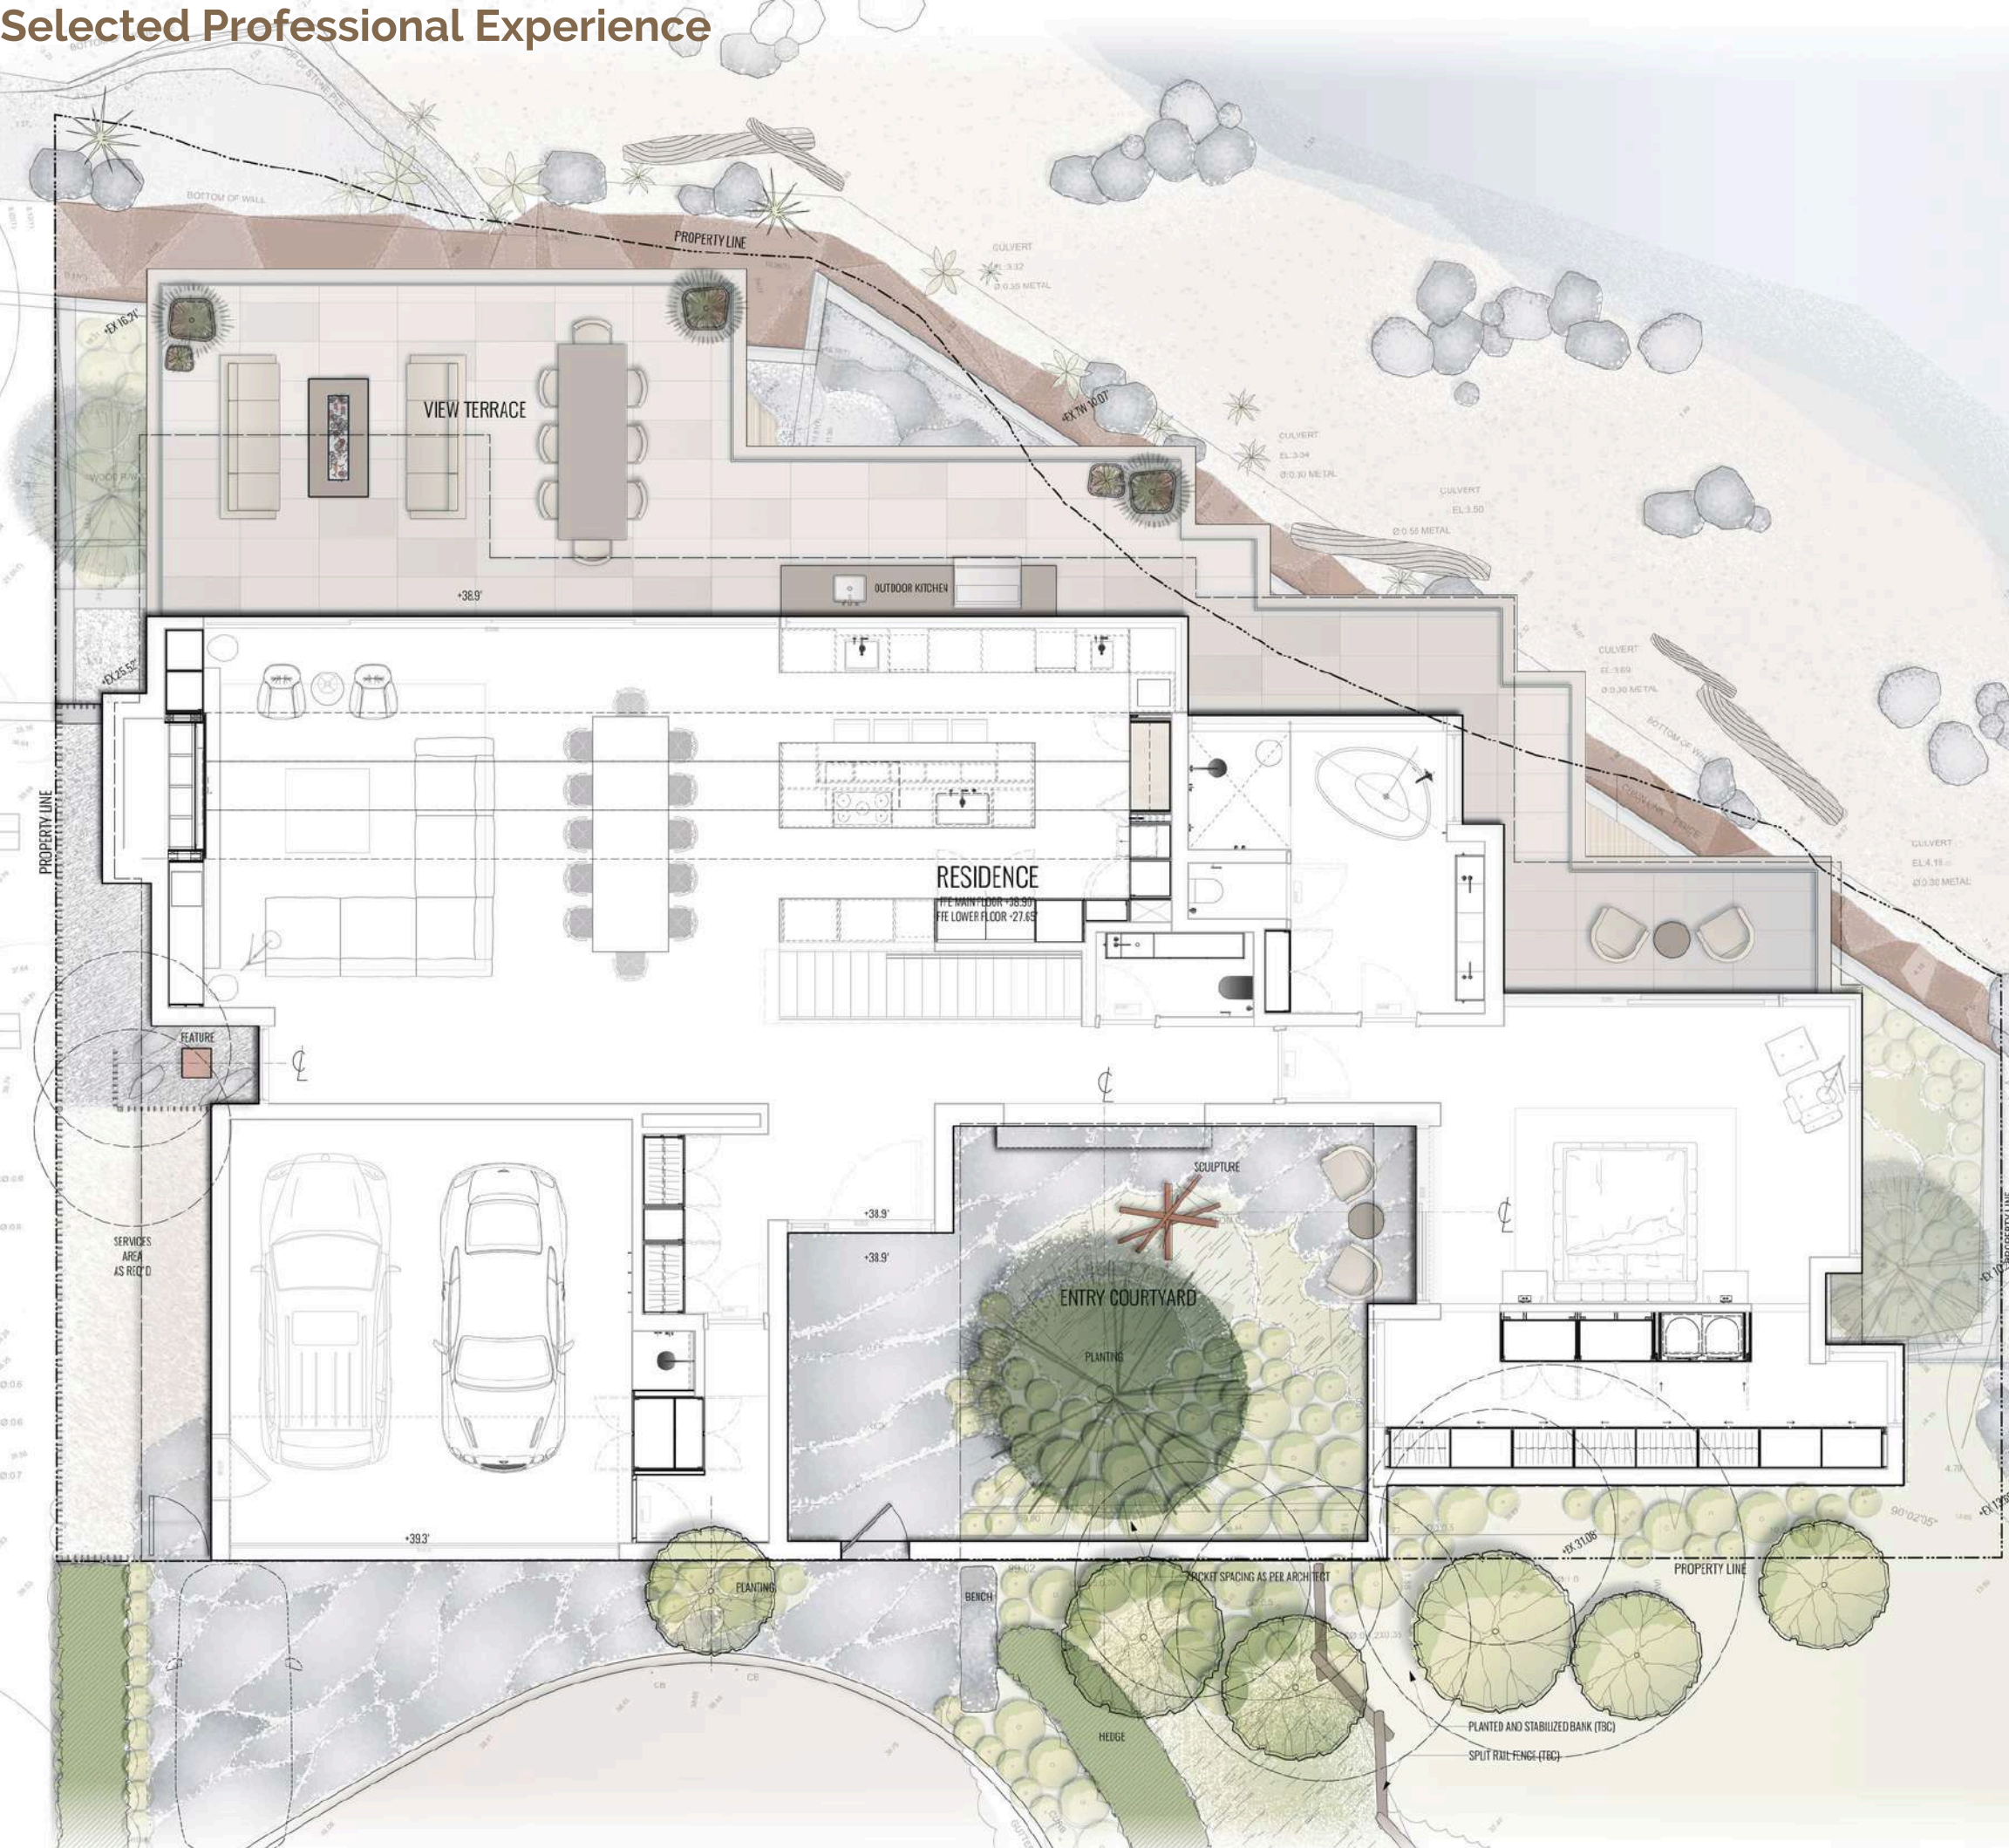


PRIVATE RESIDENCE



WATERFRONT, VANCOUVER

Project Description

Located on a sloping waterfront site, this private residence responds to the natural terrain by working with existing contours rather than altering them extensively. The house is integrated into the landscape to minimize disturbance while maximizing views and spatial quality. A generous terrace extends the living space outdoors, accommodating yoga, relaxation, and informal gatherings with direct visual connection to the waterfront.

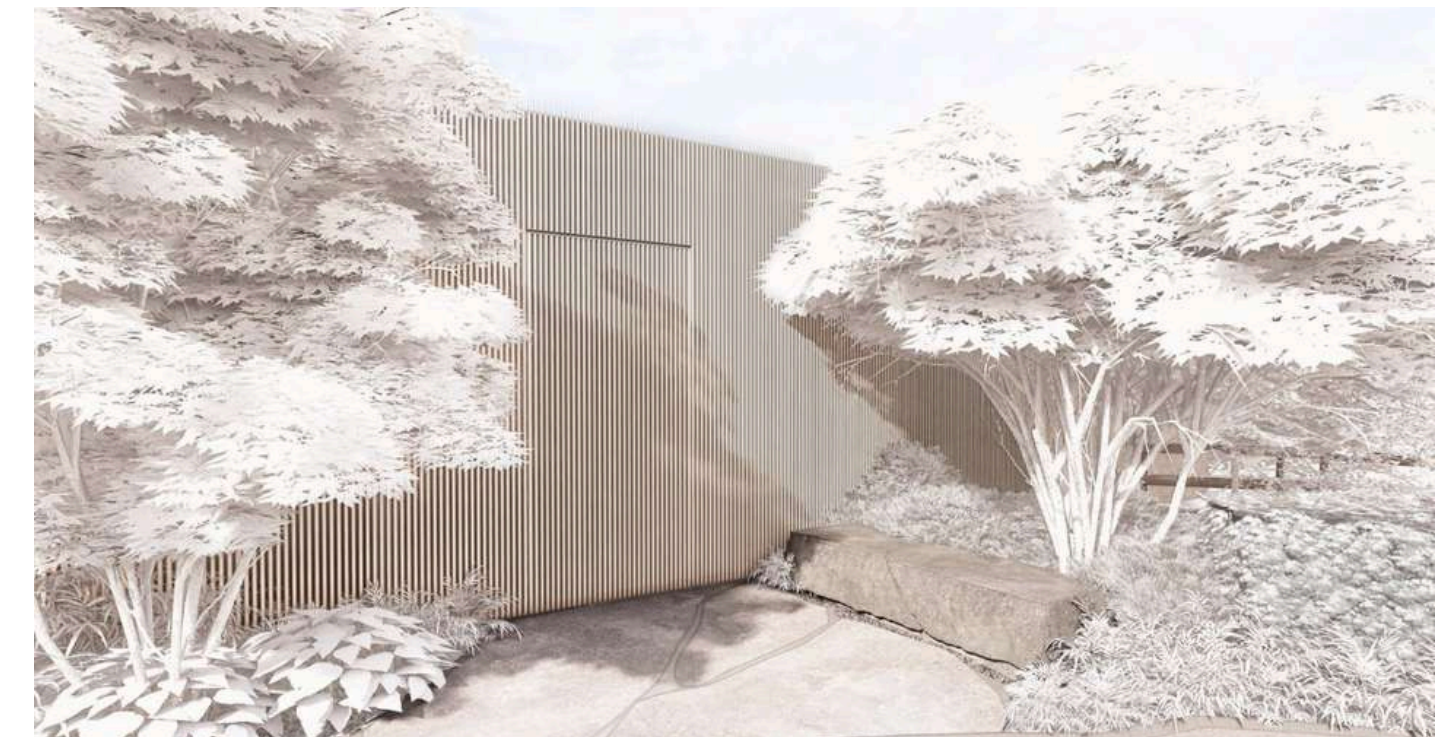


Selected Professional Experience

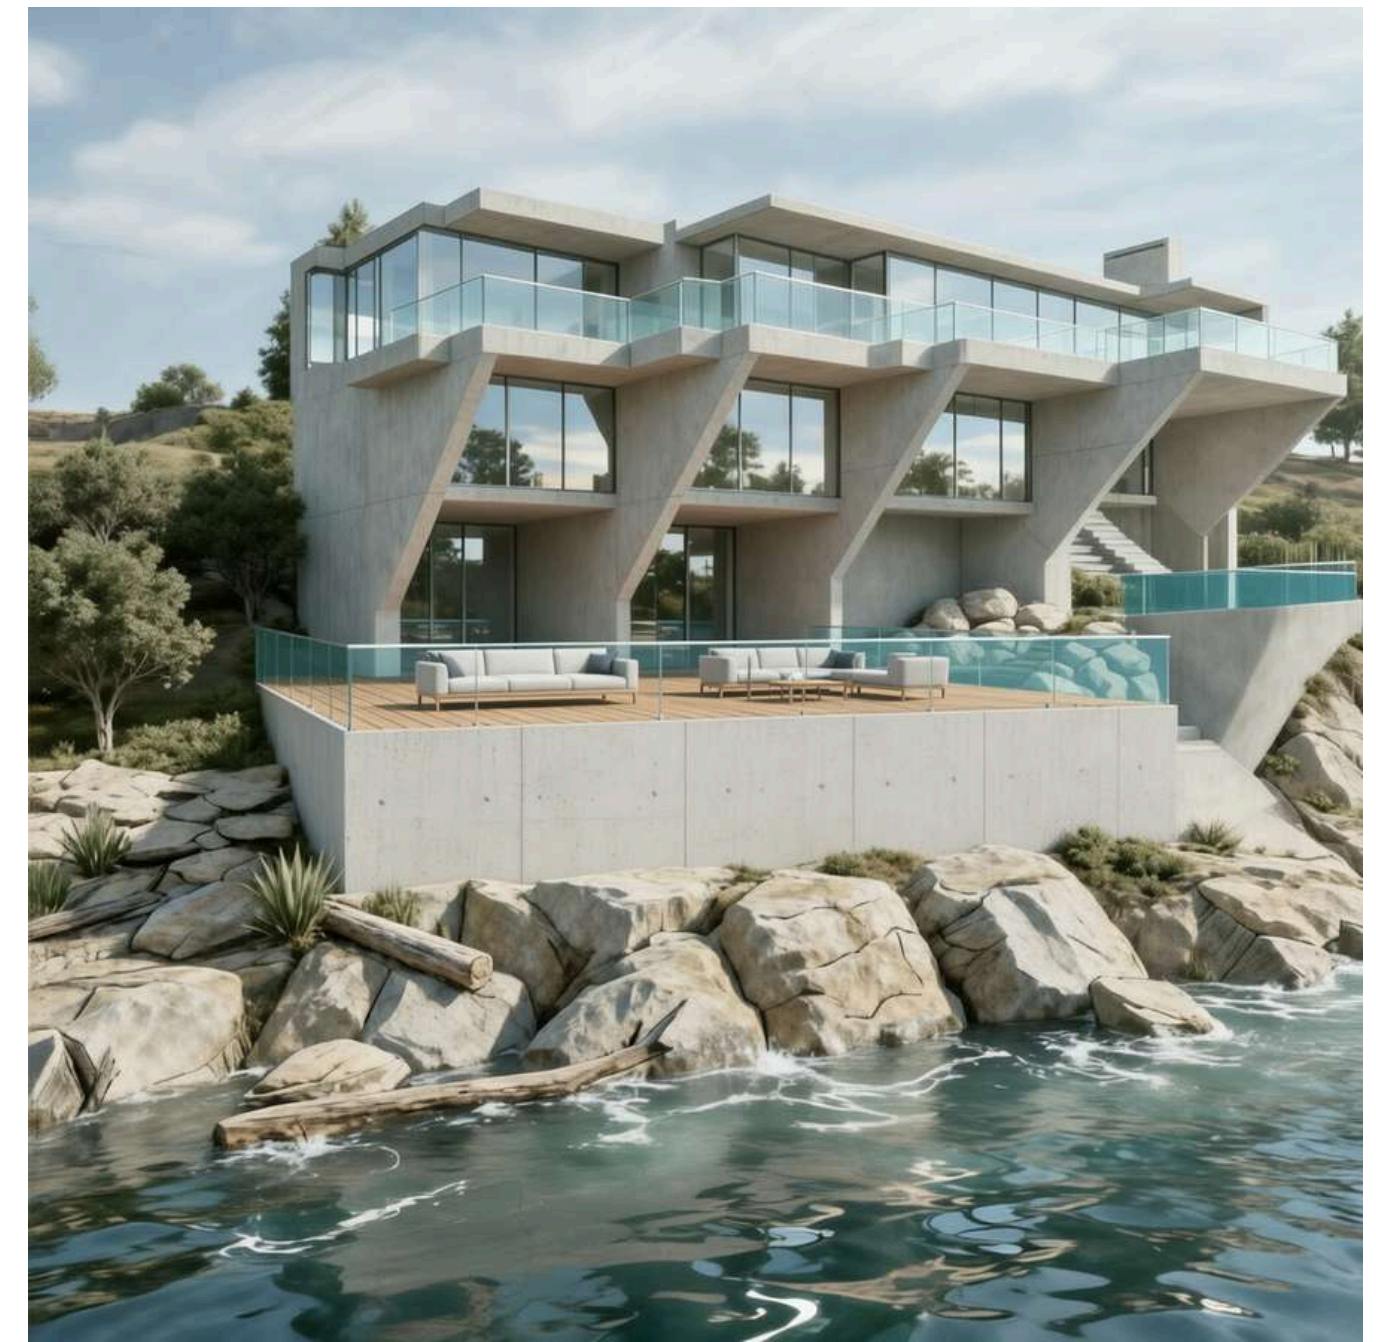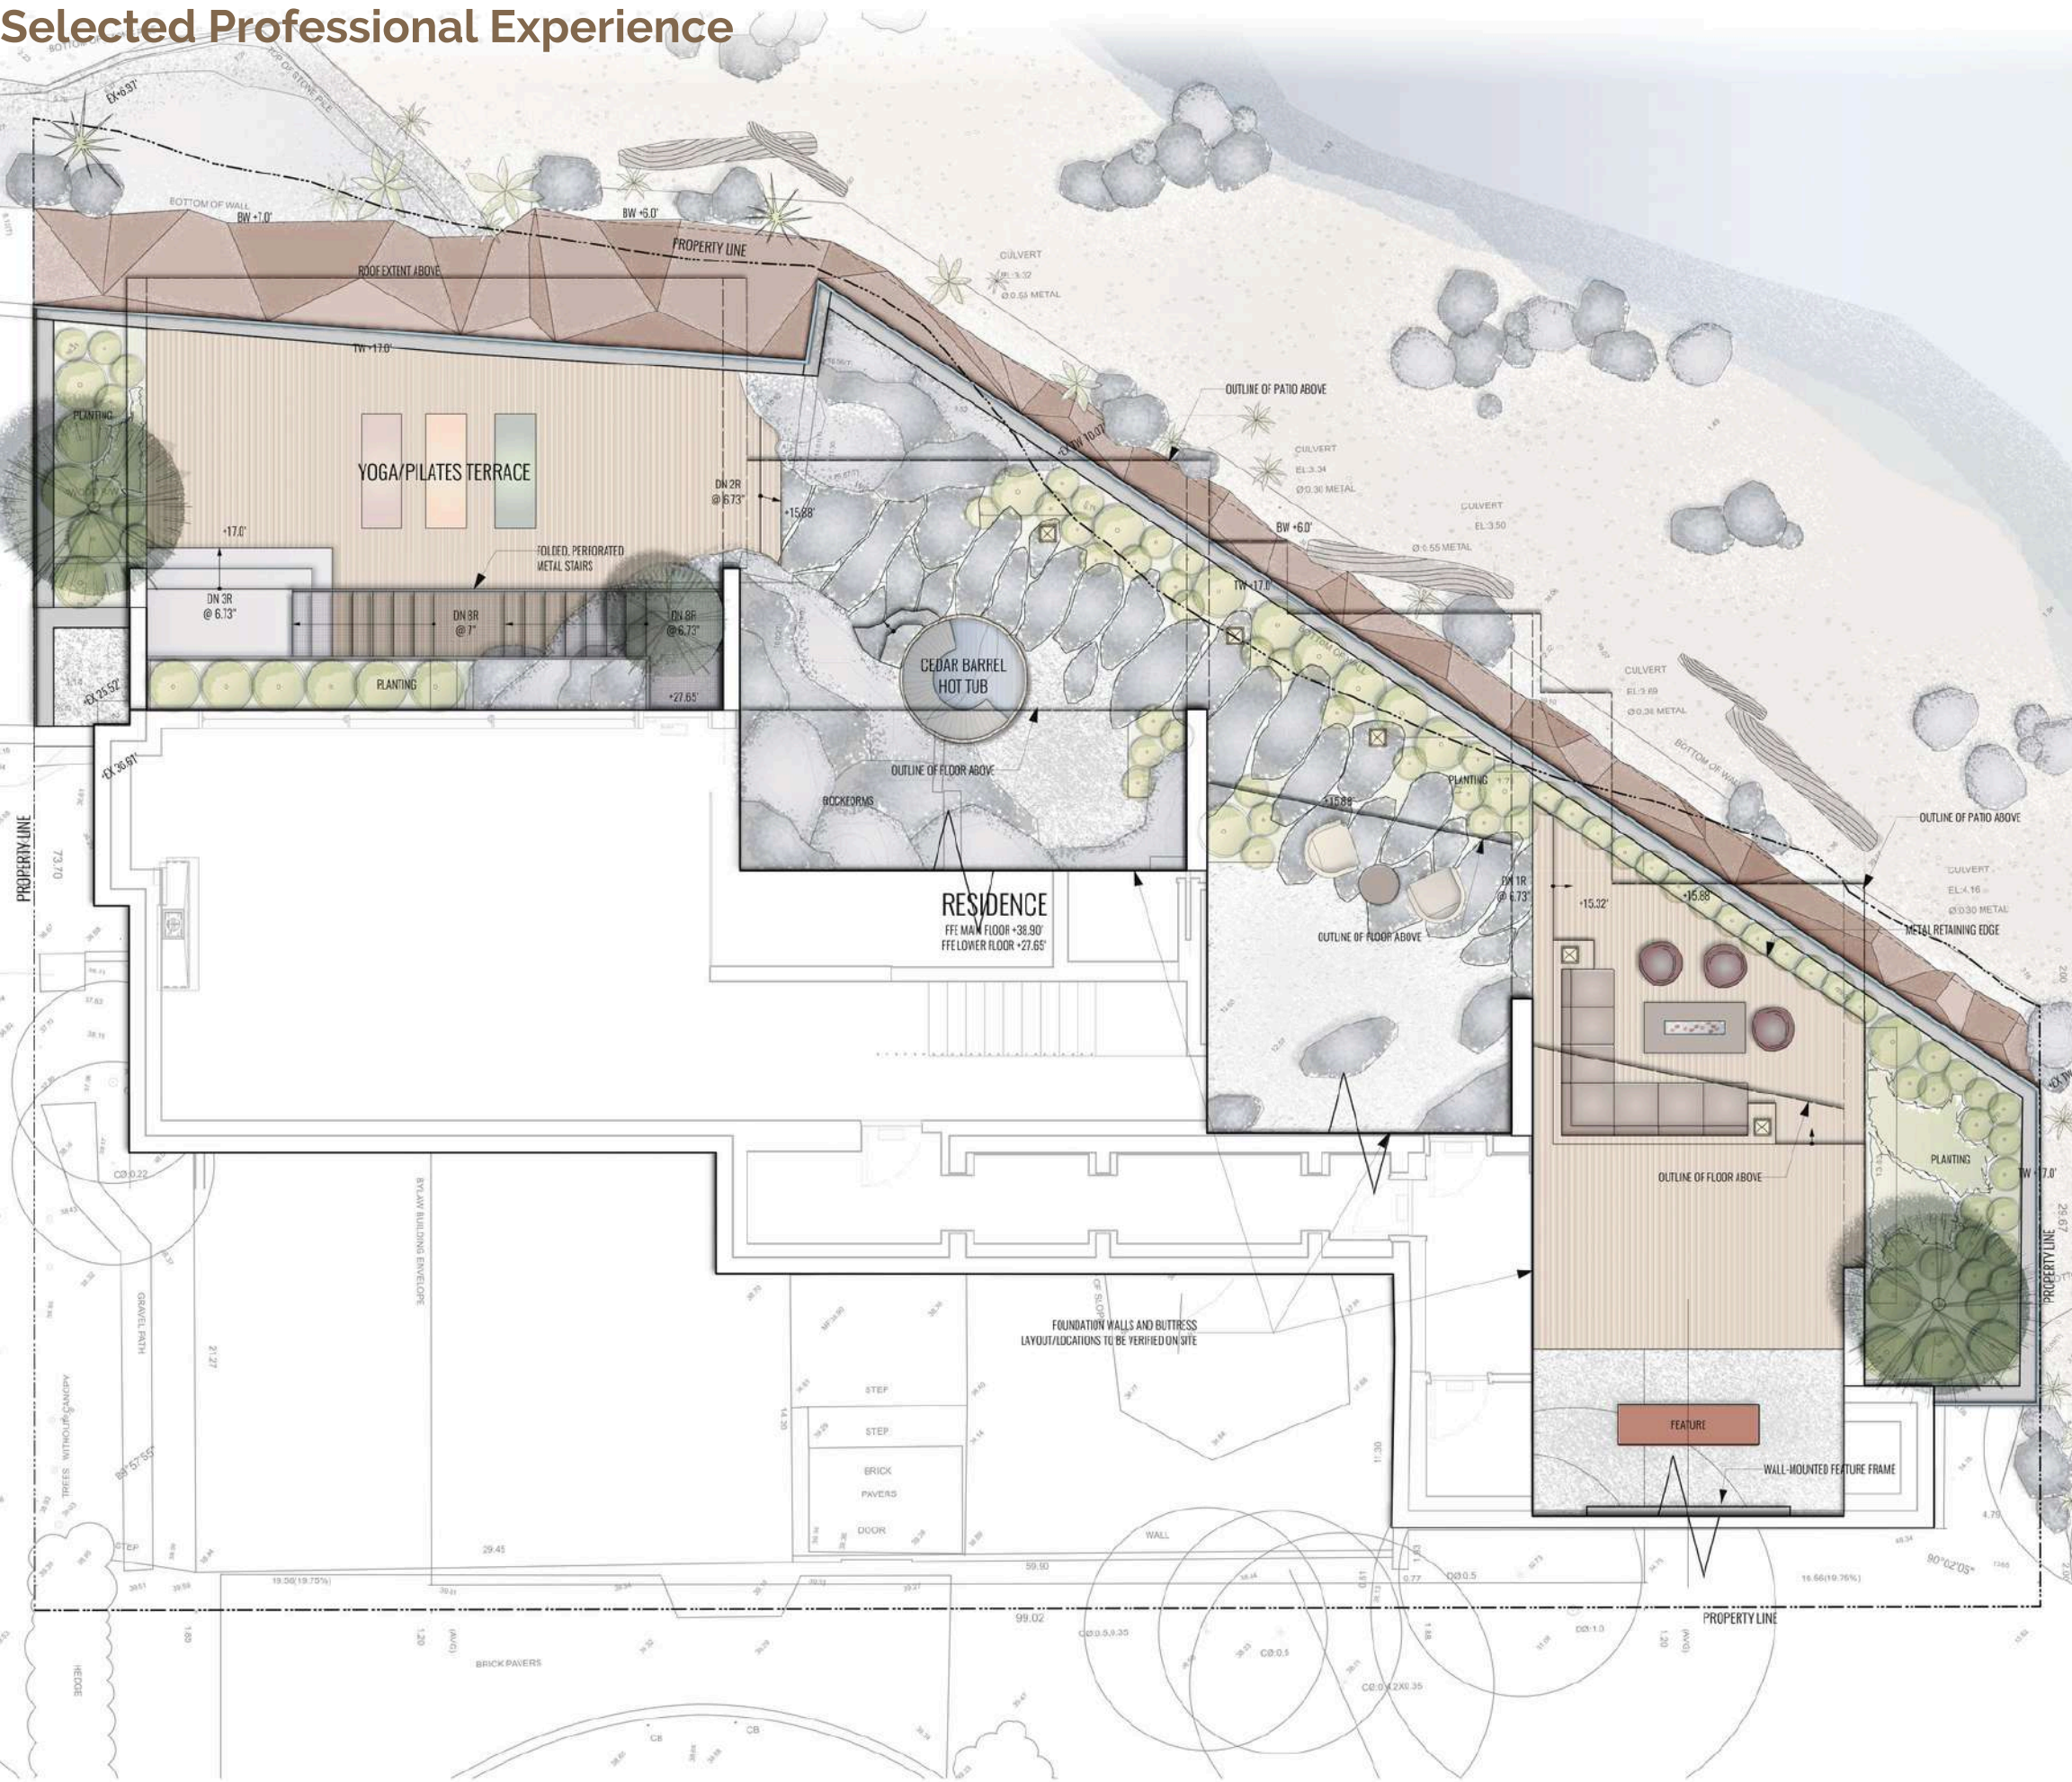

Design Rationale


The design addresses the challenge of a steep slope by retaining the natural grade and integrating boulders as part of the slope stabilization strategy, reducing the need for heavy retaining structures. The spatial layout follows the site's elevation, orienting key living areas toward the views and strengthening indoor-outdoor continuity. The project balances site sensitivity with functional efficiency and the client's lifestyle needs.

Selected Professional Experience

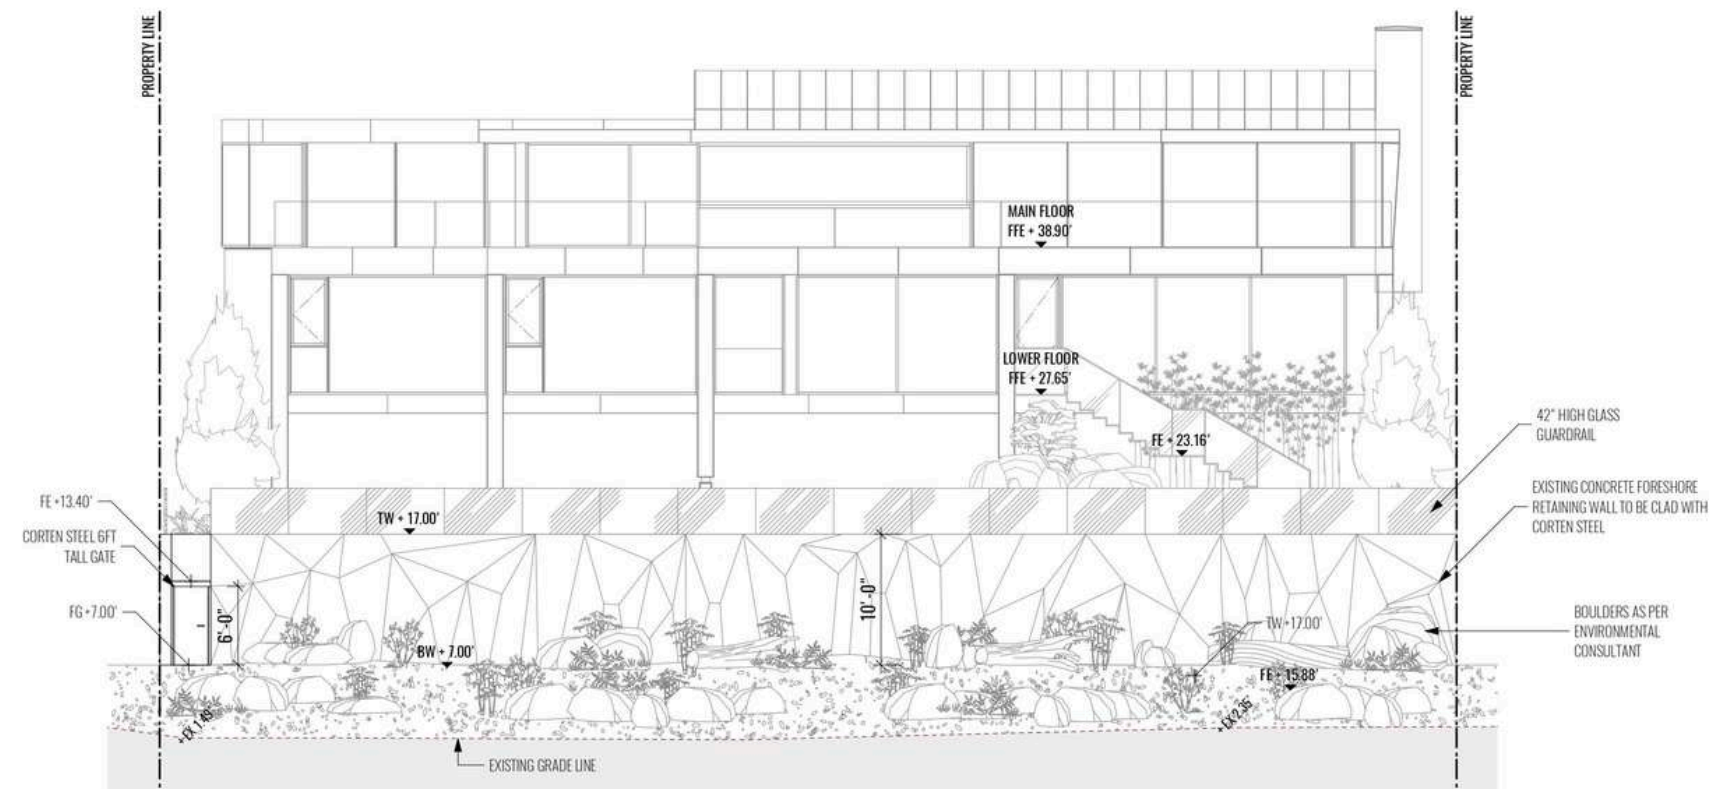

1

SECTION A
Scale: 1/8" = 1' -0"

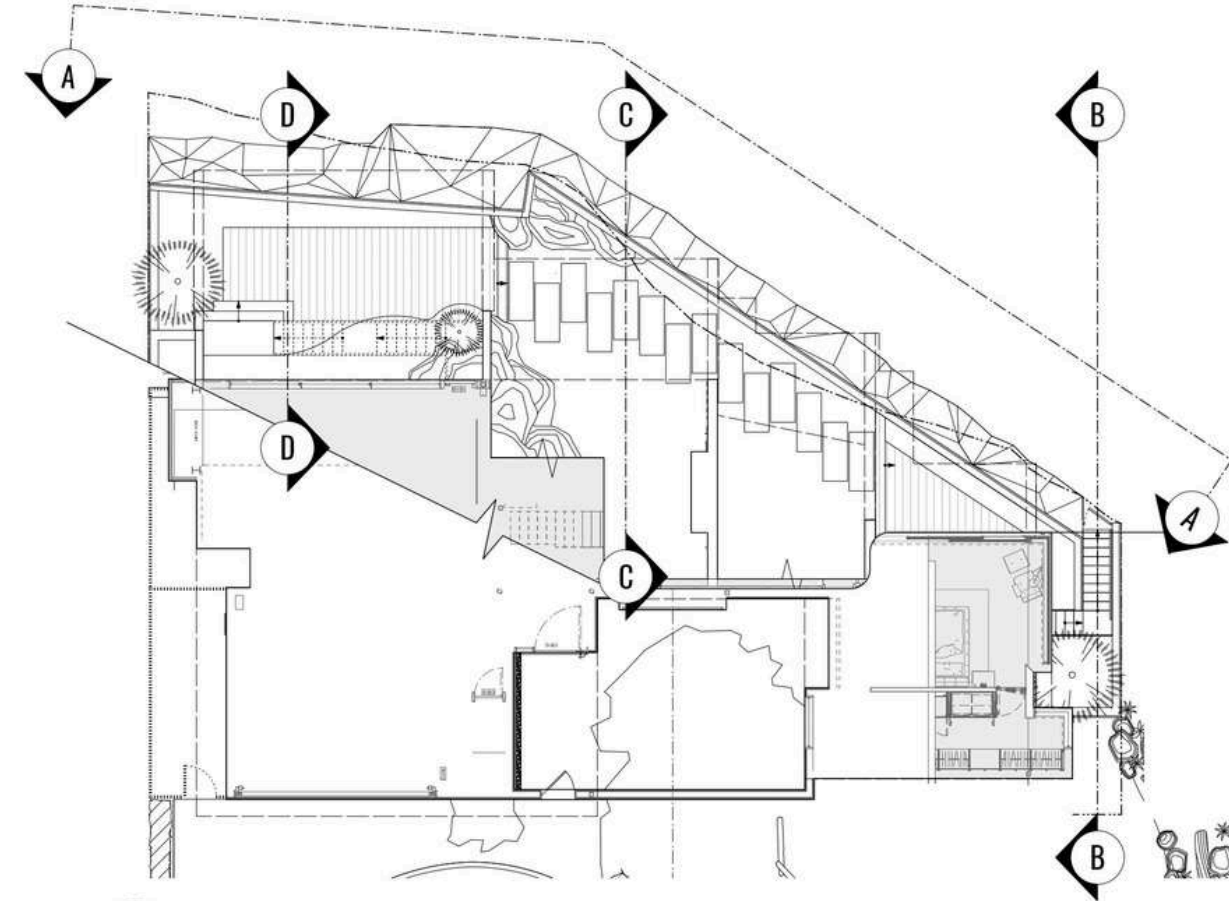


0

KEY PLAN
Scale: 3/32" = 1' -0"


Context & Site Sections

The following sections document the site's sloping waterfront topography and existing ground conditions. Understanding the natural gradient was critical in developing a design that follows the terrain, reduces excessive site modification, and integrates the building into the landscape in a sensitive manner.

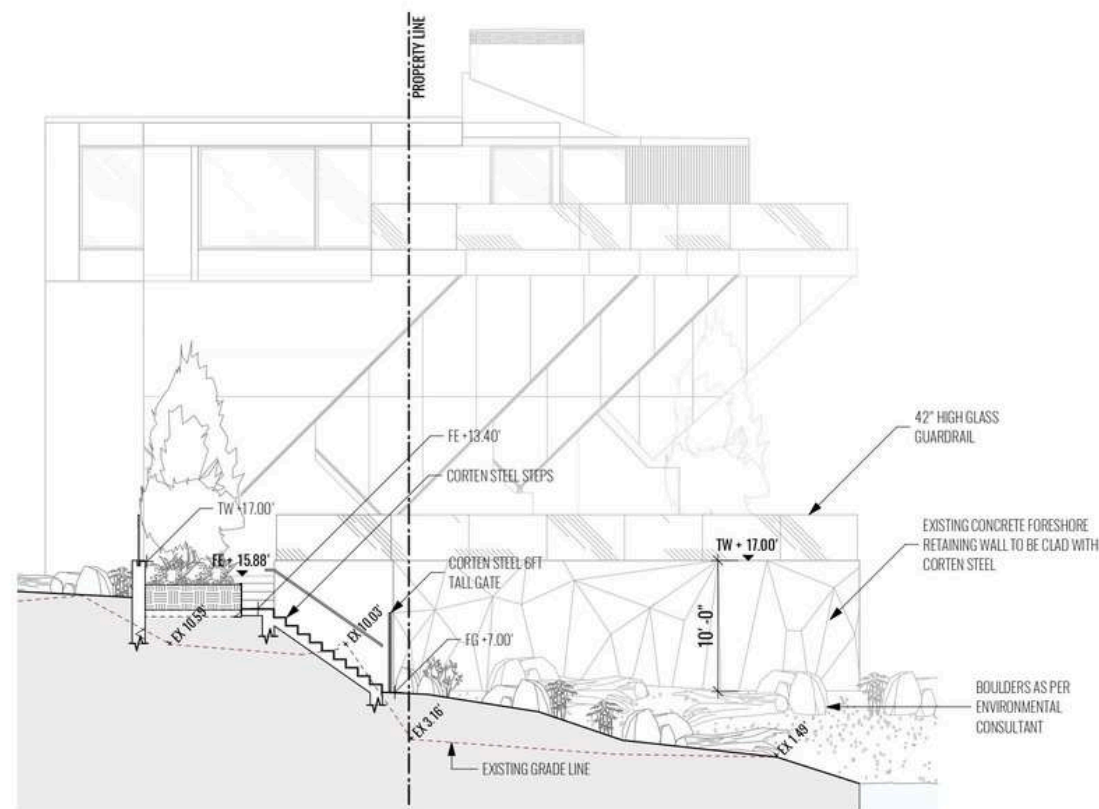


2

SECTION B
Scale: 1/8" = 1' -0"

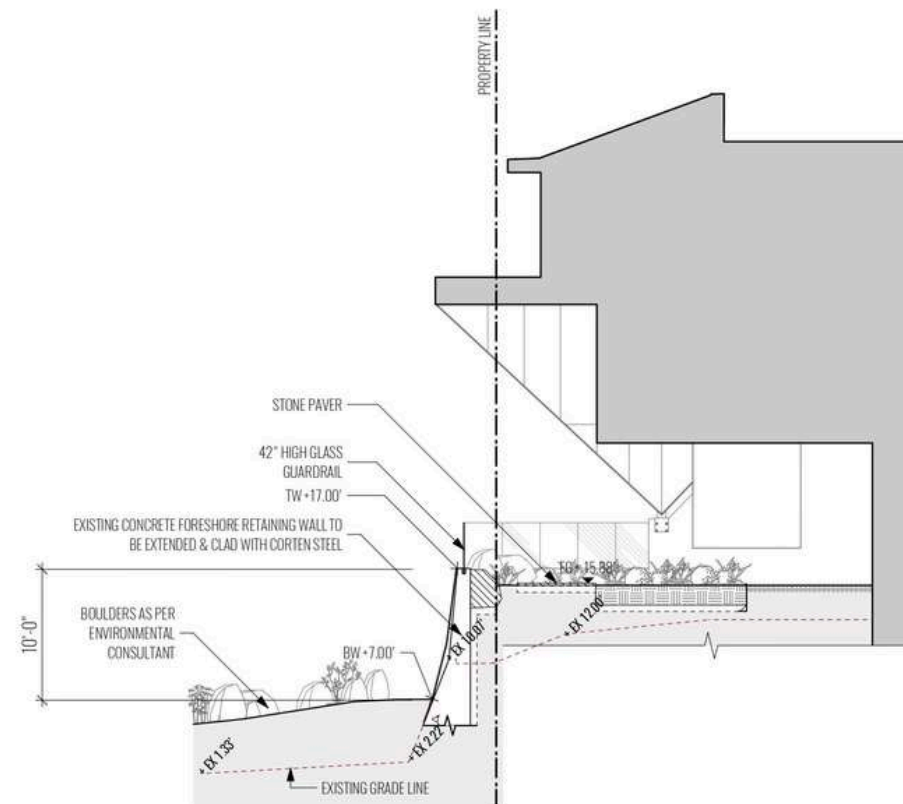

3

SECTION C
Scale: 1/8" = 1' -0"

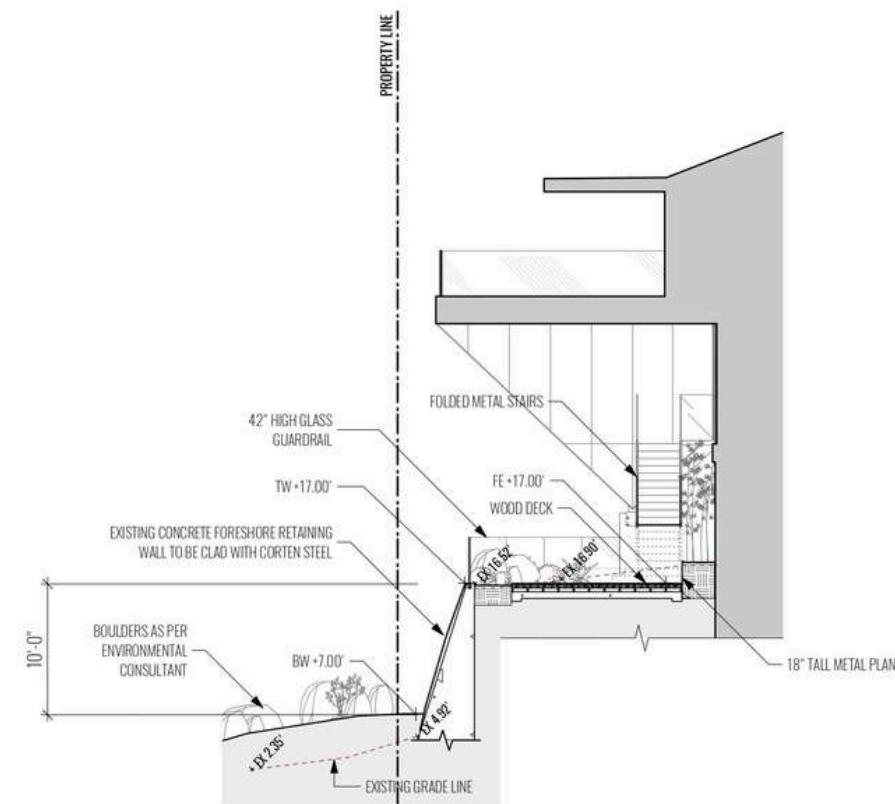

4

SECTION D
Scale: 1/8" = 1' -0"

Selected Professional Experience





PRIVATE RESIDENCE

DELTA, BRITISH COLUMBIA

Project Description

The site is organized to create a balance between private living areas and spaces for gathering and interaction. The placement of the built forms allows the main residence to maintain its privacy while still connecting to the larger landscape. Inspired by the owner's interest in nature, the site incorporates a variety of trees, natural boulders, and a pond to create a setting that feels integrated with the surrounding environment. Together, these elements shape a landscape that supports both everyday living and social engagement.

Selected Professional Experience









From Concept to Masterplan

The site is planned with a clear separation between the main house and socially interactive spaces, giving the owner privacy while keeping the two functions connected through the landscape. The areas are placed in a way that each zone has its own sense of space without feeling isolated.

The landscape plays a major role in shaping the site. Since the owner is interested in plants, different types of trees are spread across the plot to create shaded pockets and a more natural setting rather than a formal garden layout. A small pond with boulders sits within the site as a quiet focal point and helps bring a more natural character to the overall design.

Selected Professional Experience

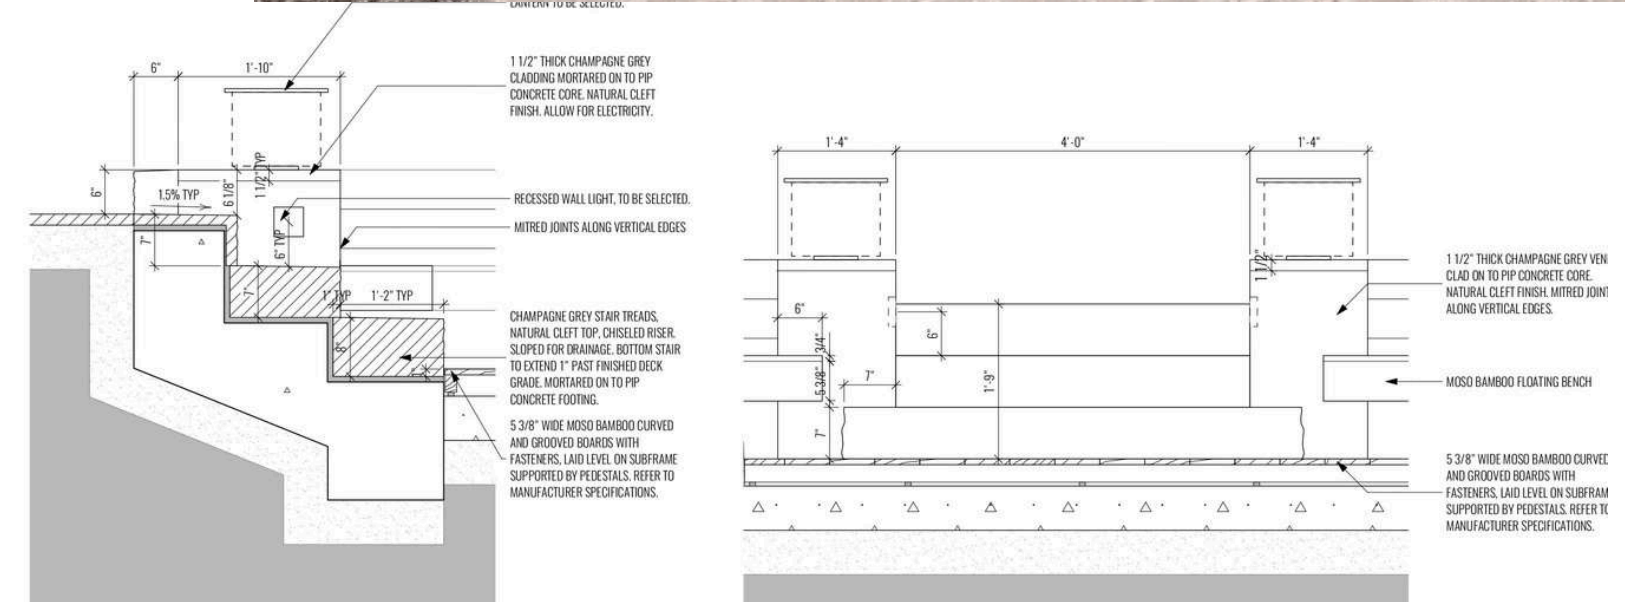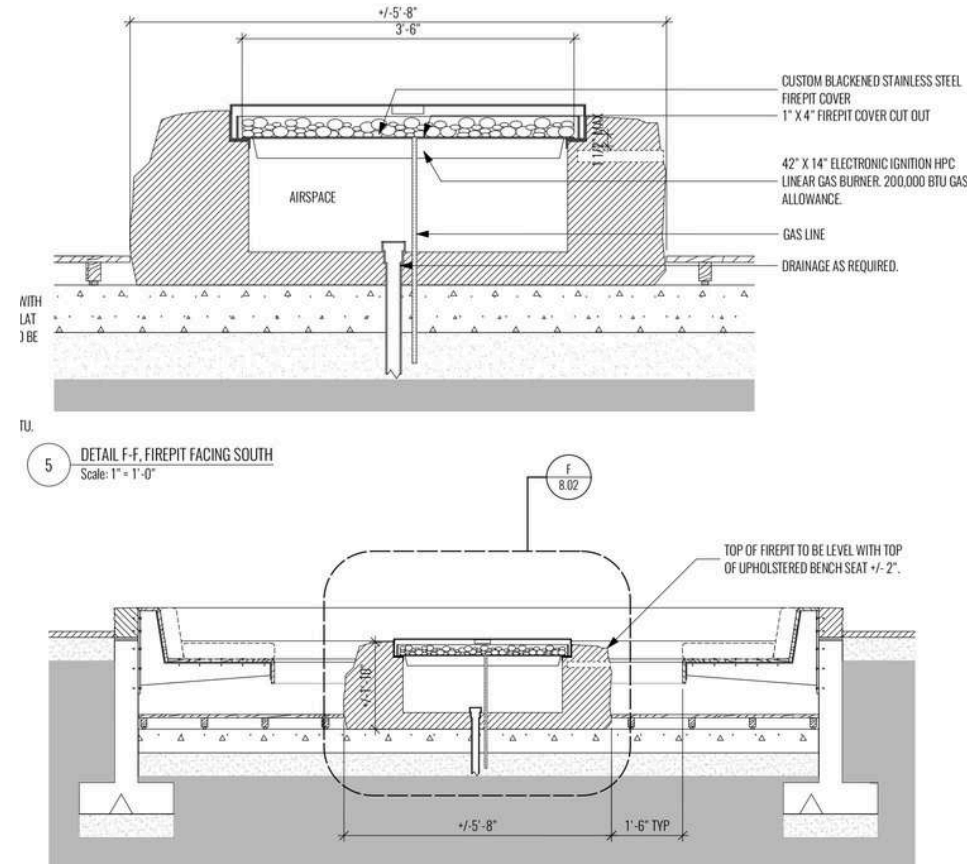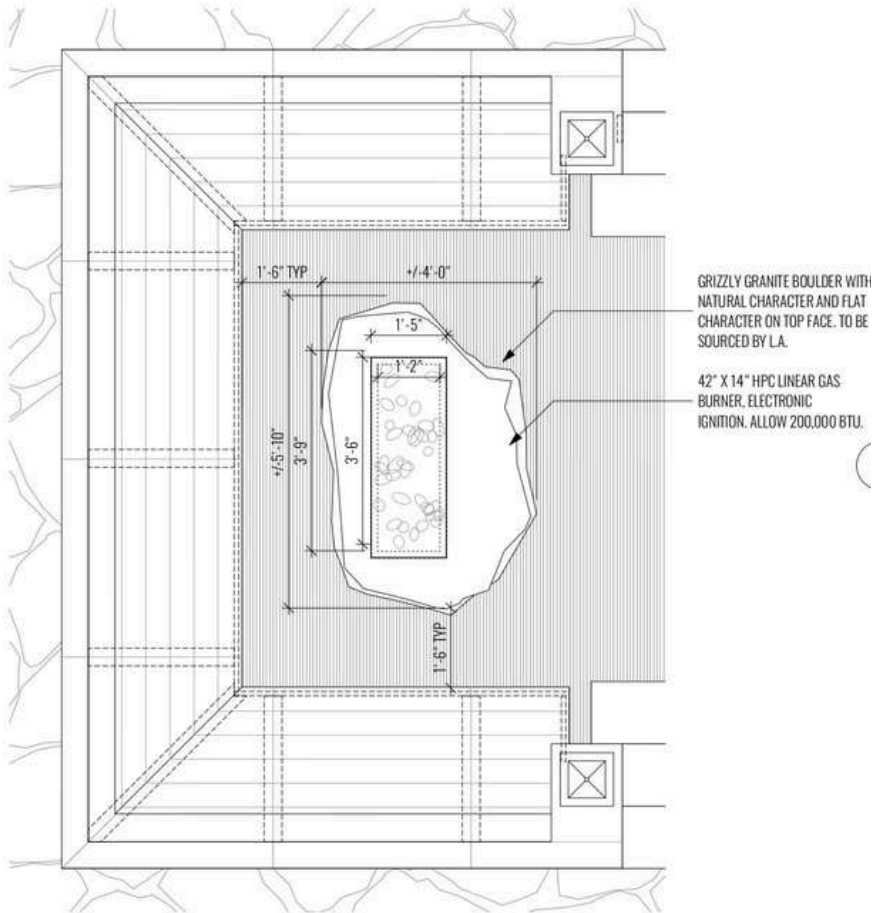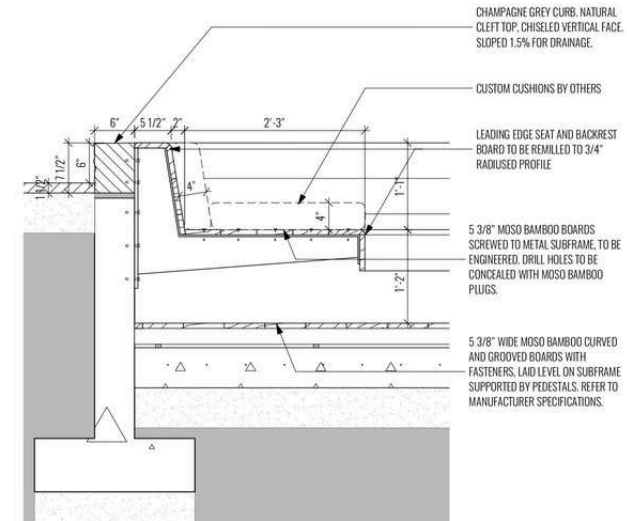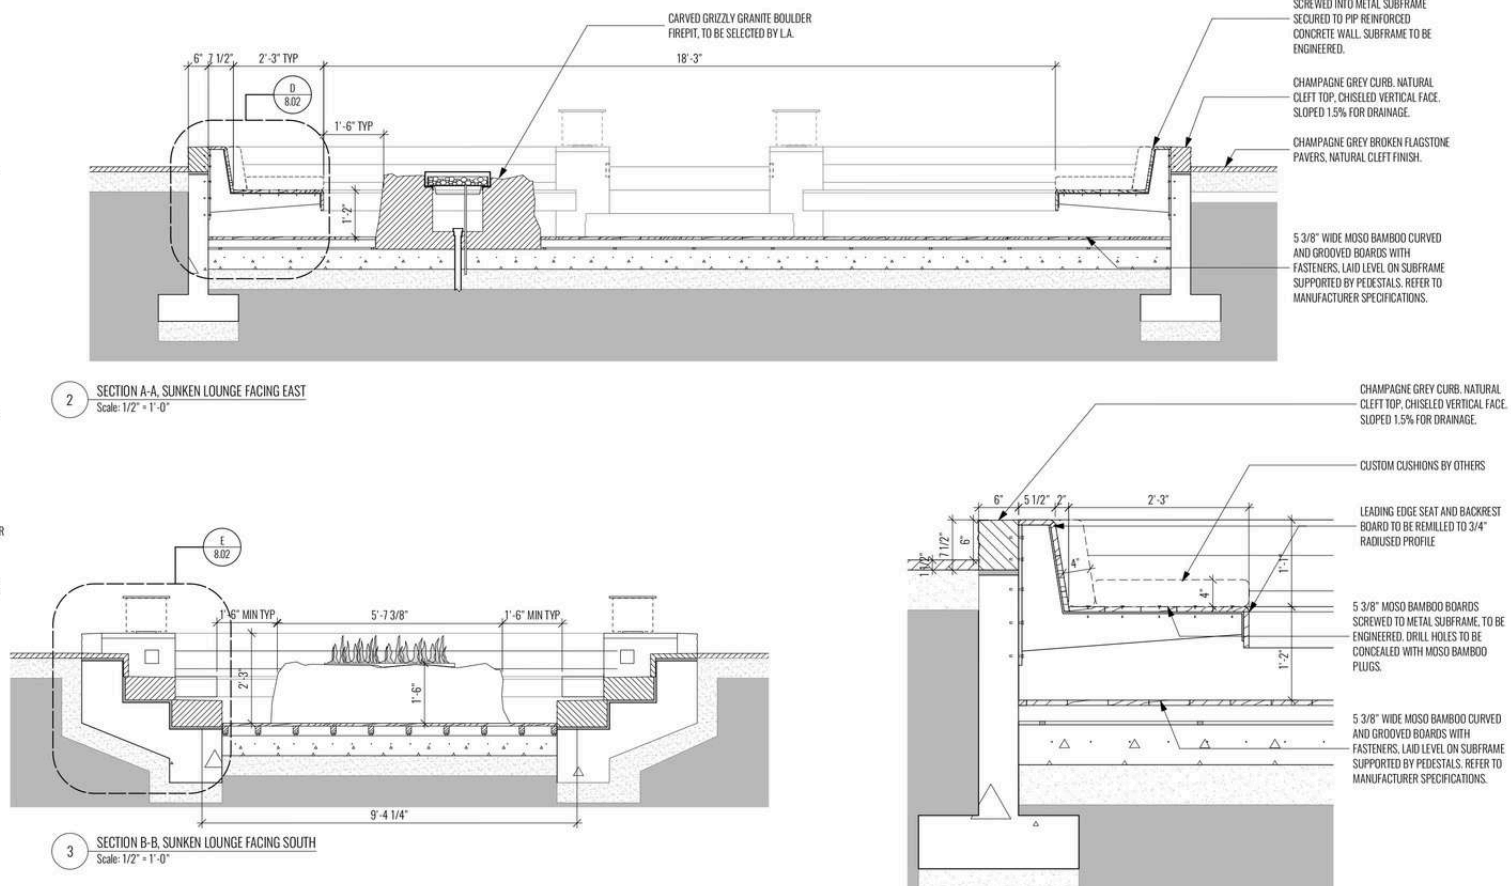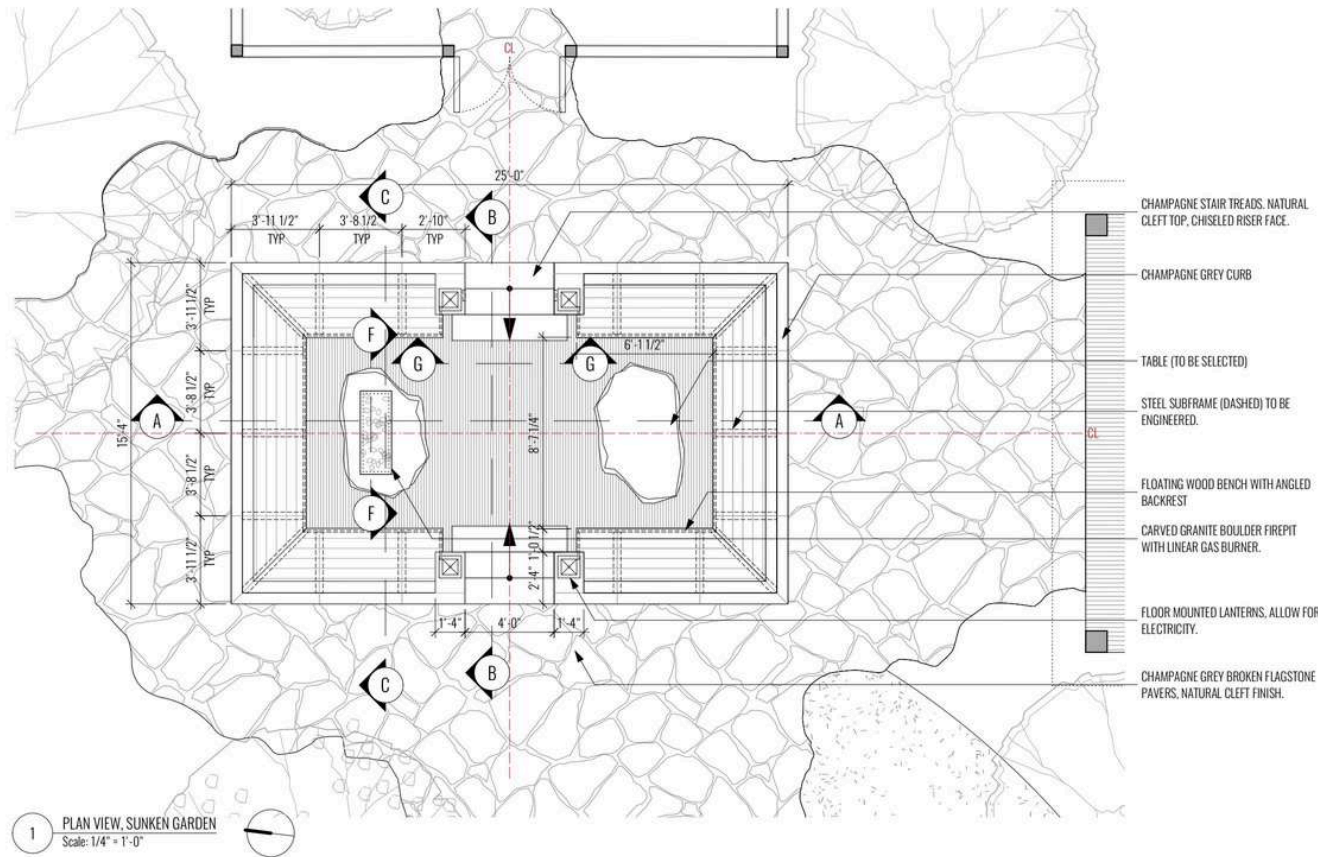

9 PLAN VIEW, FIREPIT
Scale: 1/2" = 1'-0"

6 SECTION C-C, FIREPIT FACING SOUTH
Scale: 1/2" = 1'-0"

7 DETAIL E-E, STONE STAIRS
Scale: 1" = 1'-0"

8 ELEVATION G-G, STONE STAIRS
Scale: 1" = 1'-0"

NOTE:

1. GAS SHUT OFF AND IGNITION SWITCH TO BE LOCATED NEARBY, TO BE APPROVED BY LANDSCAPE ARCHITECT.
2. FIREPIT COVER SHOP DRAWINGS TO BE PROVIDED AND APPROVED BY LANDSCAPE ARCHITECT.

Selected Professional Experience



PRIVATE RESIDENCE

VANCOUVER, BRITISH COLUMBIA

Project Description

The masterplan expresses a refined dialogue between formal architectural geometry and organic landscape composition. Axial alignments, terraced platforms, and water

elements establish order and luxury, while the lush, layered planting introduces privacy, seasonality, and a sense of immersion in nature , together producing a cohesive, high-end

residential estate where indoor and outdoor living are seamlessly intertwined.

Selected Professional Experience





INSTITUTION- GCET



GREATER NOIDA, UP

Project Description

Galgotia College of Engineering & Technology, designed by Raj Rewal, demonstrates a climate-responsive and community-oriented approach to institutional architecture. Through interconnected courtyards, shaded circulation networks, and modular planning, the campus creates a vibrant learning environment that encourages interaction while responding sensitively to the regional climate and cultural context.







Internship Work

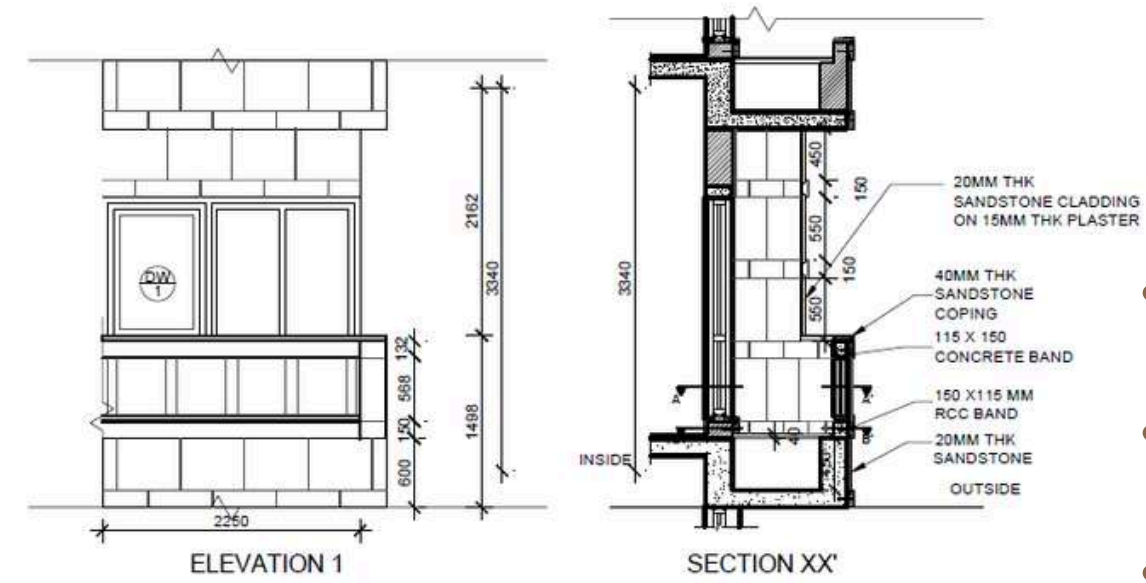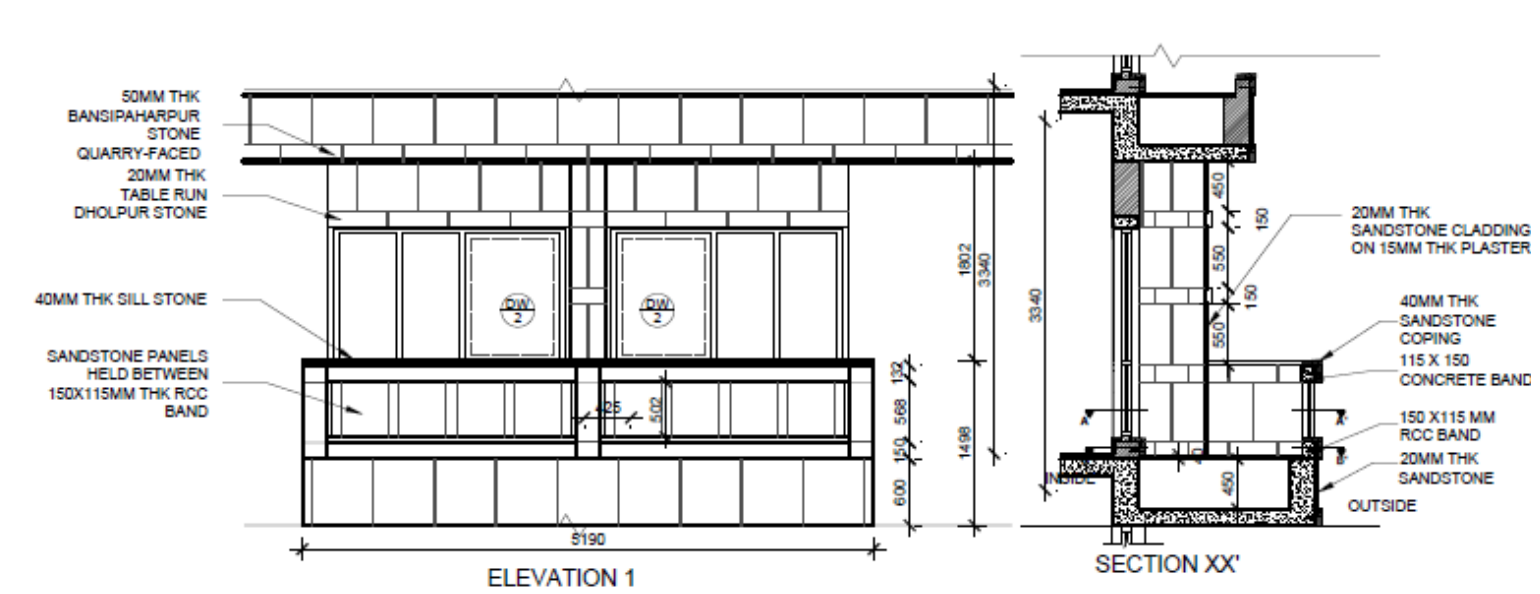

Architectural Features


- Campus planned around interconnected courtyards and open spaces.
- Climate-responsive design with shaded circulation and controlled solar exposure.
- Modular planning system allowing functional flexibility.
- Strong emphasis on pedestrian movement and social interaction.
- Integration of traditional Indian spatial concepts within a contemporary educational framework.
- Clear hierarchy of public, semi-public, and private academic spaces.

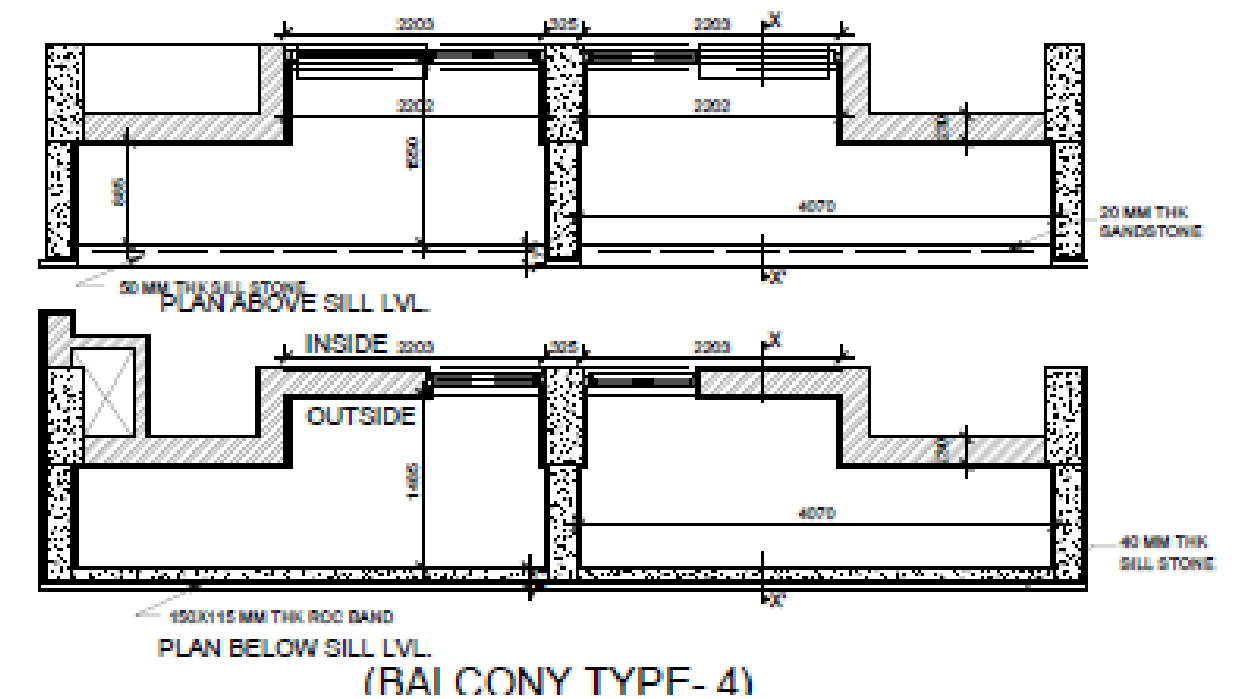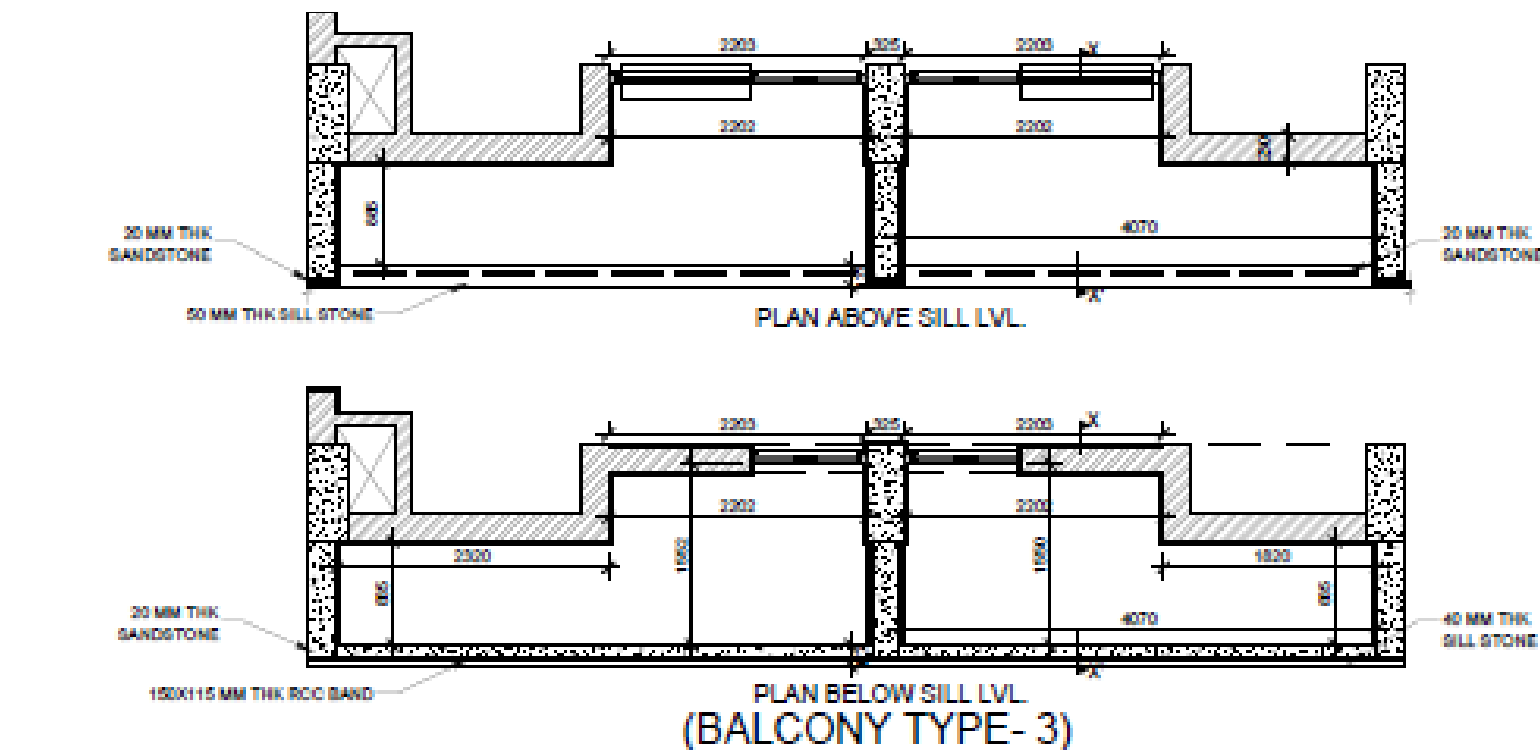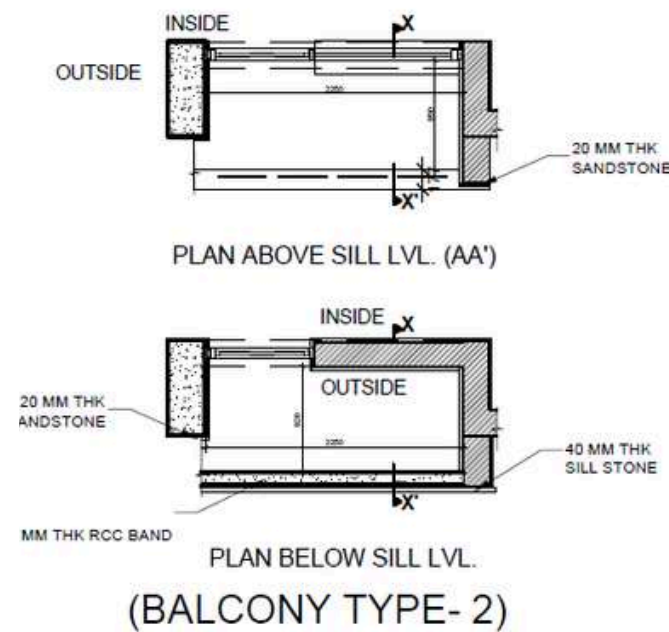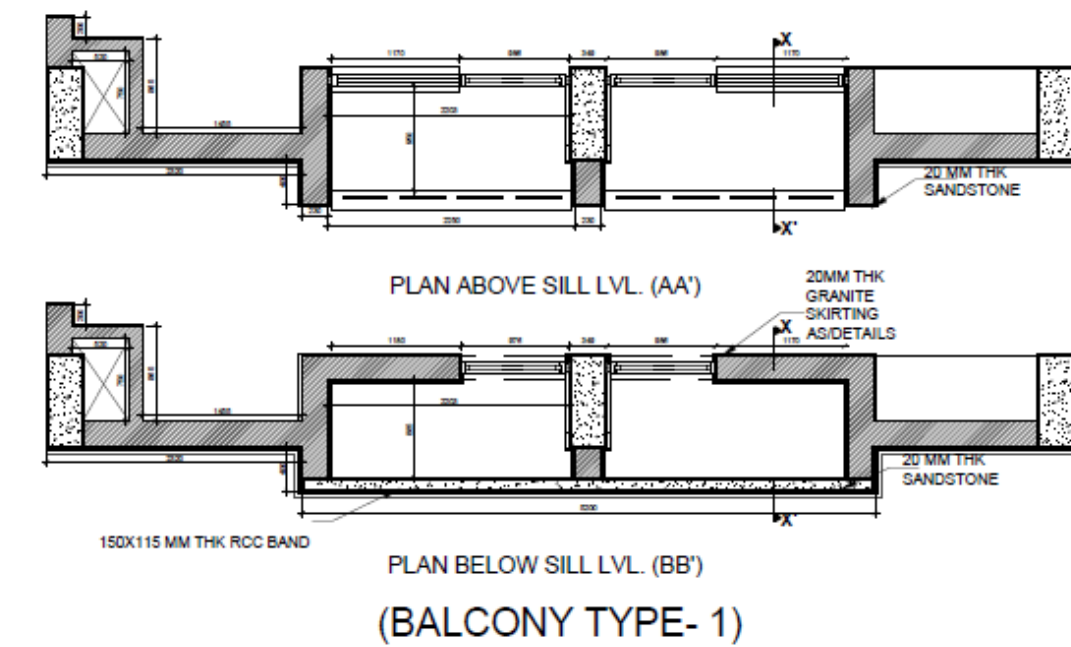



the jungle book

The design is envisioned as a space which generates an aura of serenity in the middle of a forest. The tiny library is designed at a place which is cut off from hustle & bustle of the city, at a remote area. The motive is to create a resting place for the strollers & locals, which can hold public meetings/ workshops. A true sense of living together with nature shall be experienced by the users. A learning space around trees clearly reminds of Louis Kahn who often spoke of his notion that, "the first school probably began with a man under a tree, and around him the listeners to the words of his mind."

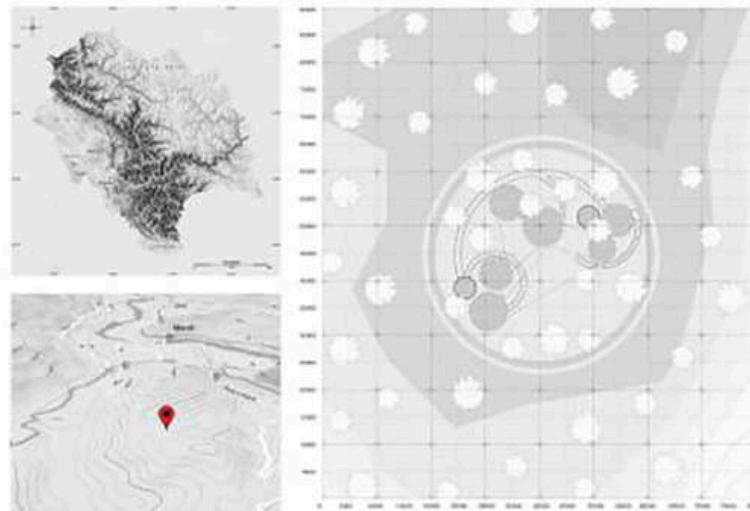


DESIGN

Carved out of forest, this library portrays sensibility, timelessness and discipline in design. In the form of cylinders, embracing an open space with a connecting staircase are arranged in the lap of nature. The Library is made with Cross Laminated Timber as the structural element. The aim of using Wood as a basic material was to bring interiors in total synergy with exteriors. Hidden deep in the dense vegetation, it is designed to have minimal impact on its stunning surroundings. It should incorporate a variety of spaces and areas that support readers' comfort and most importantly, bring the community together for shared experiences. The fundamental rule is that a simple shape is much more sustainable than a complex shape. Hence, cylindrical spaces are introduced that uses Wood as main material for construction. To ensure interaction of community, all the 3 trees supporting cylinders are interconnected with stairs that form a complex within.

- LEDs
- Green Roof
- Rainwater Harvesting
- Light Weight
- 360° View
- Solar Panels
- Modular
- Scenic

CLT FOR CONSTRUCTION





The production and use of cement is responsible for approximately 8% of the world's CO2 emissions, which will continue to increase if current construction trend prolonged. One of the most effective and eco-friendly alternative is CLT, which can save an average of 45 tons (40 tonnes) of CO2 per dwelling. CLT allows us to construct lighter, better quality buildings, more quickly, with reduced foundation. These timber must be extracted from sustainably grown forest.

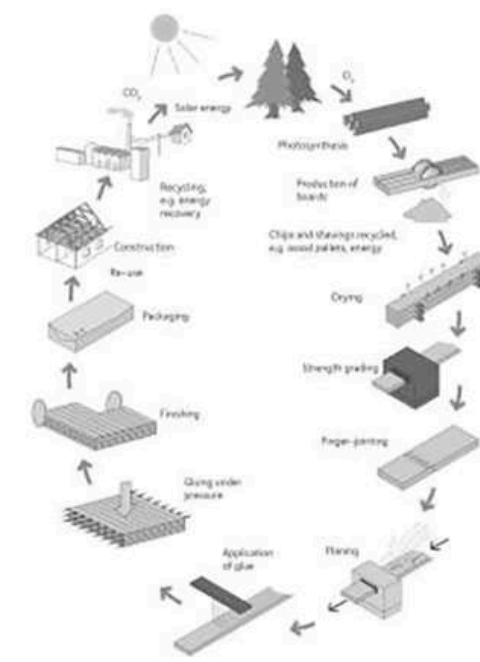

ADVANTAGES OF WORKING WITH CLT

- Increased Speed of Construction
- Raw Material Fully Fossil-free
- Carbon Sequestering
- Weather Resistant
- Light Weight and Strong
- Off-site Construction
- Reduced Labor Costs
- Seamless in Millimeters
- Improved Safety

VZTLB98792

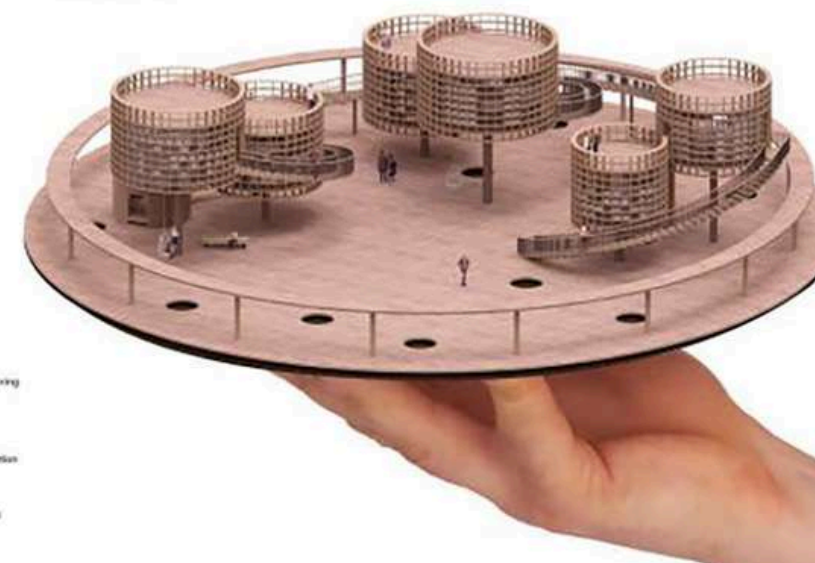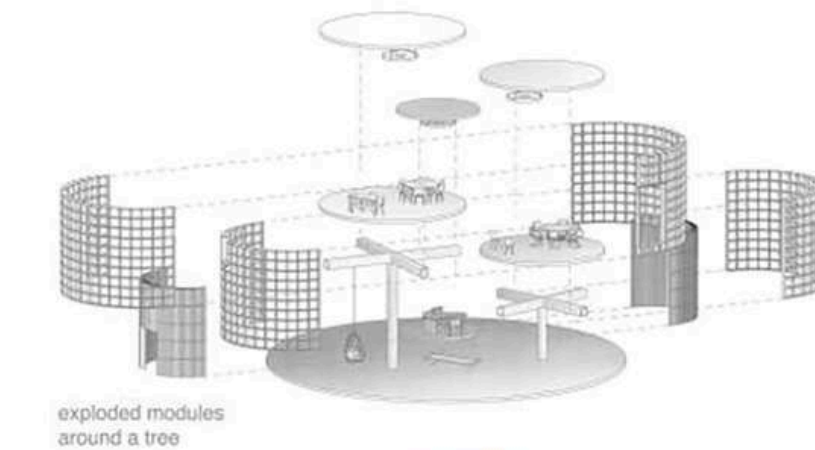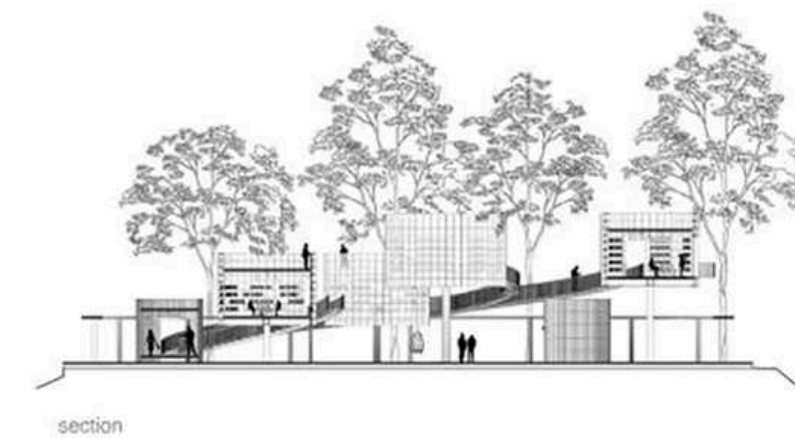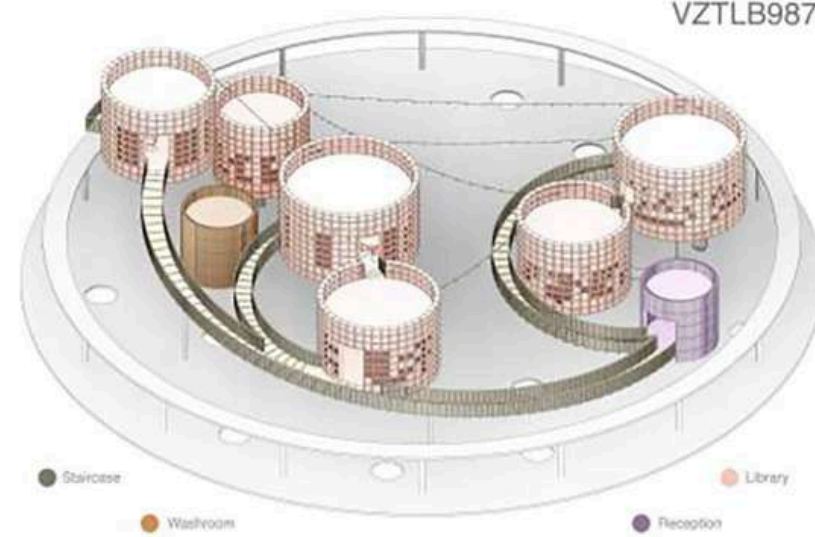

TINY LIBRARY

Freelance Design Project



Project Description

Site Area : 2500 sq.m.

Ground Coverage : 498 sq.m. (20%)


The spatial organization is guided by natural principles—flow, rhythm, and organic continuity rather than rigid geometry. The plan unfolds as a sequence of immersive zones, where dining areas are interspersed with interior gardens and planted courtyards. These green pockets act as spatial anchors, allowing guests to experience nature as an active participant within the dining environment.

FORMAL DINING




Four flip flop seating in dining area

- POLISHED CONCRETE
- PINE WOOD TABLE
- RED WOOD CHAIR
- FABRIC

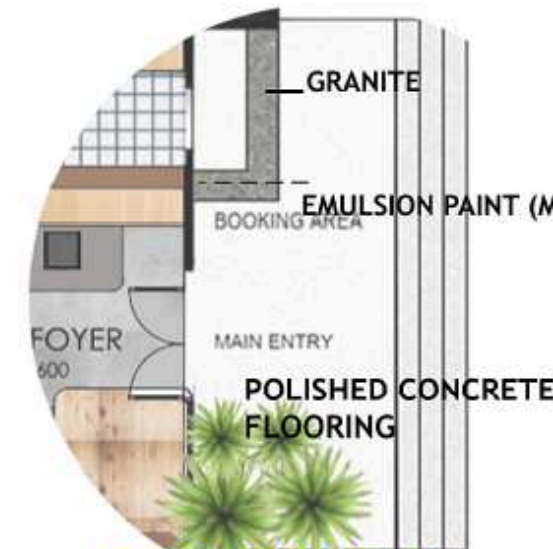


COUNTER TEXTURES

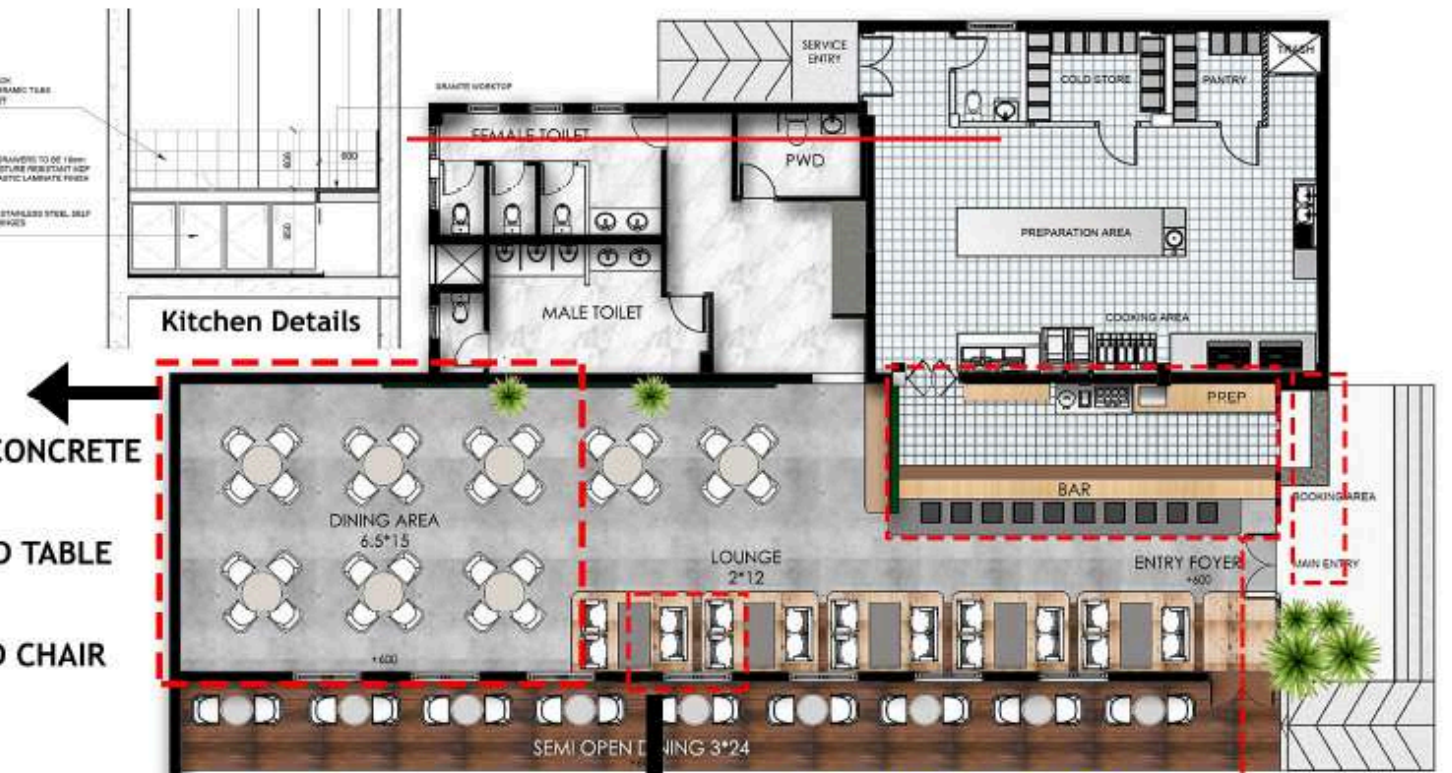

LOUNGE

- PINE WOOD FLOORING
- GRANITE TABLE TOP
- LEATHER
- RED WOOD CHAIR

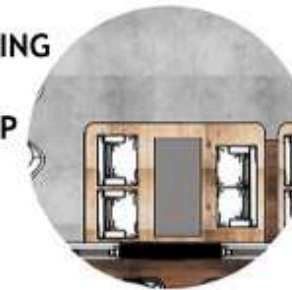

Sofa seating in lounge

BAR AREA TEXTURES

	NAME	USE	COMPANY	FEATURES
	Polished Concrete	Flooring	AZTEC	Polished concrete has, over the last decade or so, become one of the most popular flooring solutions available in today's marketplace due to its affordability, ease of maintenance, efficiency, cleanliness, and ability to aesthetically fit into both industrial and post-industrial environments.
	Cement Stone	Counter slab	Seti Exports India Pvt. Ltd	- Highly Durable - Hard Wearing & Resistance To Staining - Excellent Insulator - Looks like Granite
	Redwood	Bar Table	Century	- Redwood is one of nature's strongest materials. - It is a much lighter. - It has natural texture that help making it durable. - It is sustainable, renewable, recyclable. - It has a gorgeous color.
	Pine wood	Bar Cabinets	Century	- It has excellent strength and lines. - It gives a rustic look, natural and rugged look. - More resistant to staining and swelling. - It is strong and durable.
	Emulsion Grey (Matt)	Ceiling		It has higher coverage compare to most other paint.
	Emulsion White (Gloss)	Walls		- Water resistance and washable after the first three to four. - Much suitable for latex paints.
	Green walls	Partitions, Walls		A living wall consists of successive panels of plants growing vertically. They are usually attached to an interior/exterior wall or fence structure. However, structures can also be free-standing.

